


LTA NORTE-NORDESTE 1 E 2 88kV

APROVADO

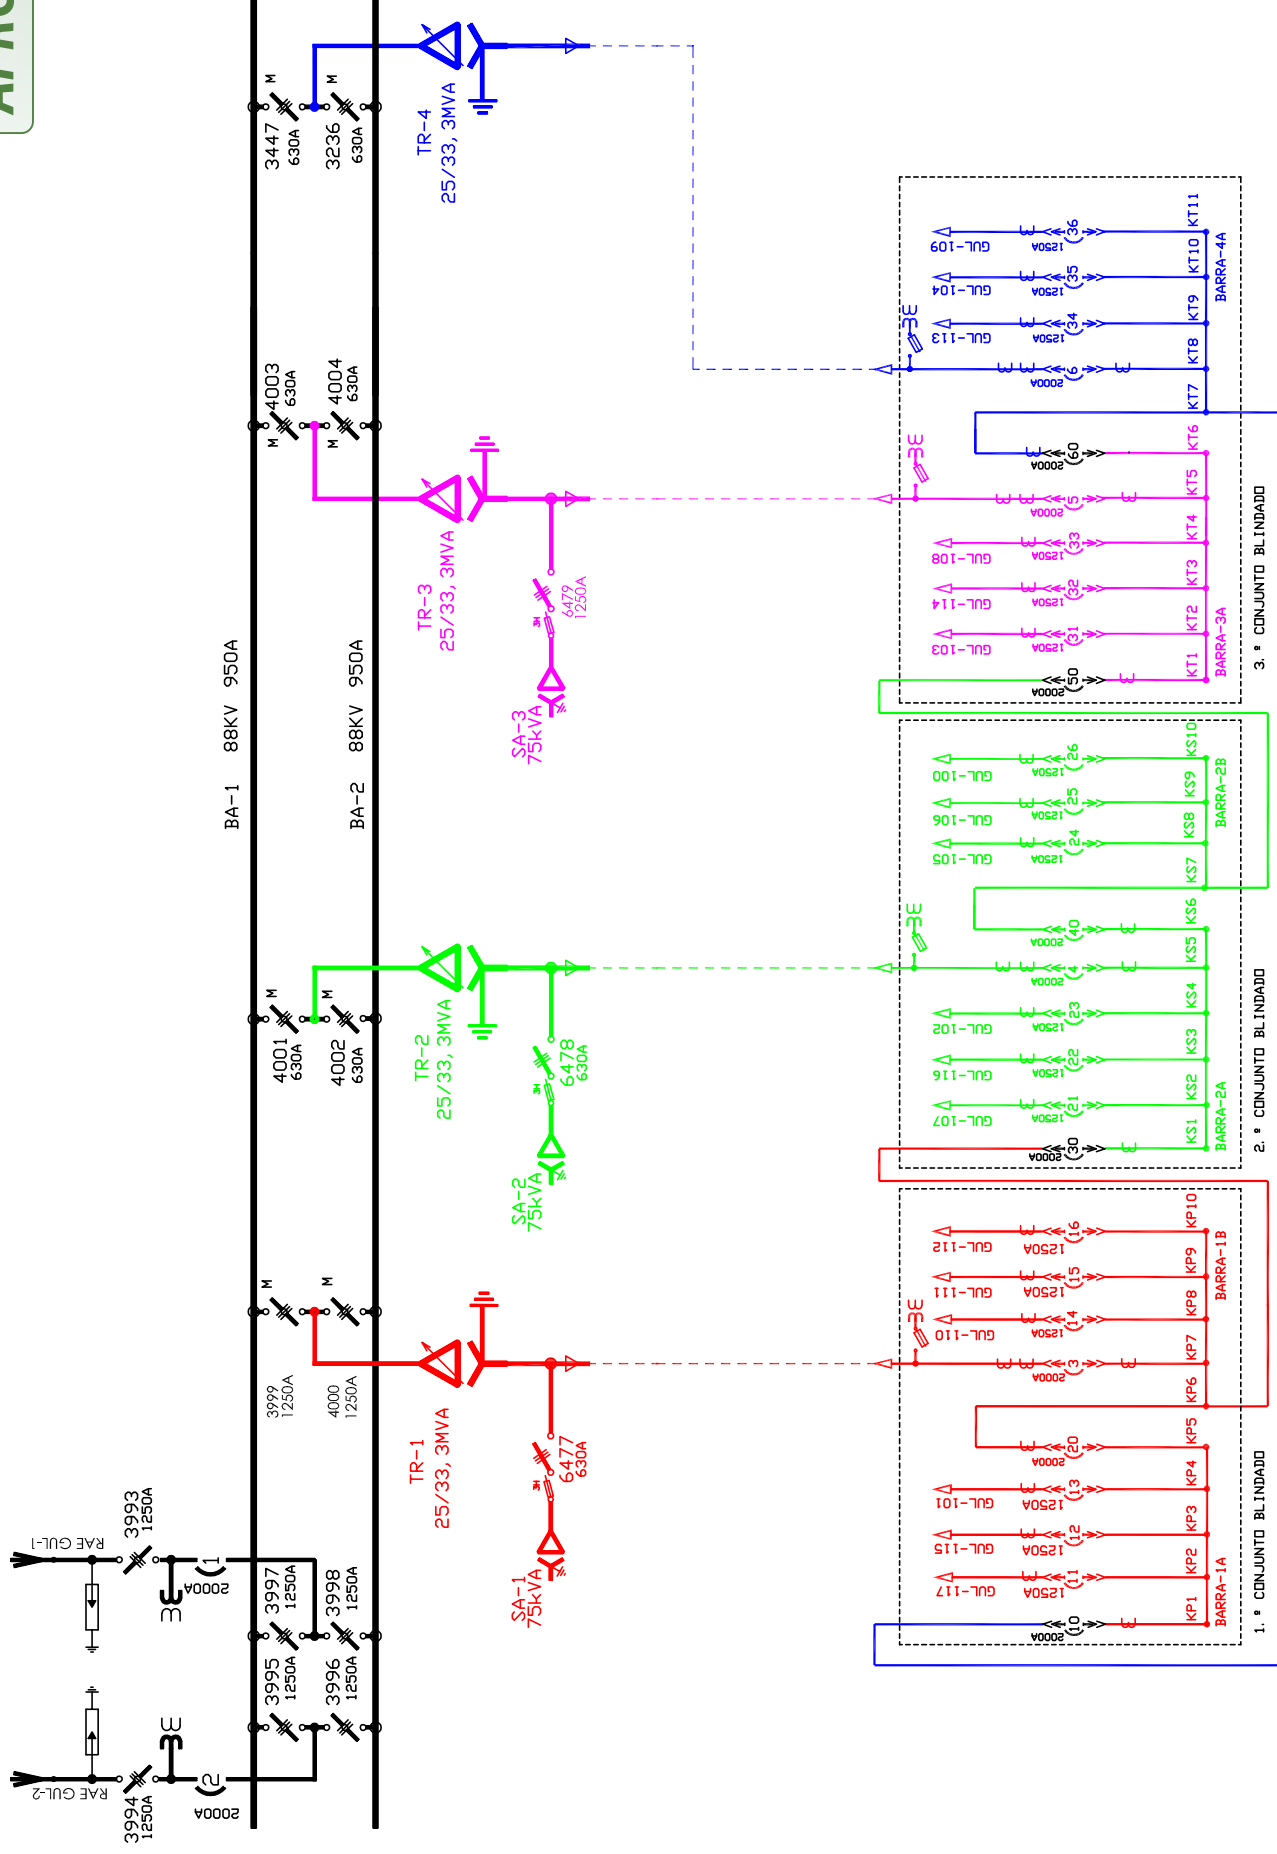

NOTAS:
1) TENSÃO DA BATERIA 48V.C.C.
2) ALARME REMOTO P/ COS

24	INCLUSÃO DO NOME DA INHA
----	--------------------------

23	CORREÇÕES DAS CORRENTES DAS SEC.'S 3999 e 4000
----	--

22	INSERÇÃO DAS COORDENADAS
----	--------------------------

21	CORREÇÃO GERAL
----	----------------

	0	1	2	
--	---	---	---	---	---	---	---	---	---	---	----	----	-----	-----	

DSS	25/04/17
-----	----------

DSS	29/03/17
-----	----------

gpp	27/01/15
-----	----------

10/11/10	ENERGIZACÃO: 02/03/1074
----------	-------------------------

[illegible]

●

DPS-BD - SISTEMAS DE CONTROLE

TEL: 0333 2440 444

DIAGRAMA UNIFILAR SIMPLIFICADO

ETD GUARILLHO⁹

LAT -23.46826

LON -46.5148

DATE: 01/01/2017